

MATIÈRES DANGEREUSES
VEUILLEZ NOTER QUE LE LOCATAIRE ET L'(LES)ENTREPRENEUR DU LOCATAIRE DOIVENT, LORS DE LA MISE EN CHANTIER ET DE L'EXÉCUTION DES TRAVAUX DE CONSTRUCTION DANS LES LOCAUX ,SE CONFORMER À TOUTES LES EXIGENCES RELATIVEMENT AUX LOIS APPLICABLES SUR LES MATIÈRES DANGEREUSES . DE PLUS, LE LOCATAIRE N'AUTORISERA AUNEC MATIÈRE DANGEREUSE DANS LES LOCAUX PENDANT LA DURÉE DU BAIL.

L'ENTREPRENEUR DU LOCATAIRE DEVRA GARDER AU CHANTIER UNE COPIE DES PLANS ANNOTÉS ET APPROUVÉ PAR LE BAILLEUR POUR LA DURÉE DES TRAVAUX DE CONSTRUCTION SUR LES LIEUX.

LÉGENDE			
		NO. DU DESSIN	
		PAGE DU DESSIN	

NO.	DATE	REVISIONS	PAR

NOTES GÉNÉRALES:

Ces dessins ne pourront être utilisés pour la construction que s'ils sont approuvés par le client.

Le contracteur et les sous-contracteurs désignés devront vérifier toutes les dimensions sur les lieux .les détails et spécifications des dessins et rapporter tous les changements aux designers avant les travaux.

La conception ,les idées et la création ,de même que les dessins et spécifications s'y rattachant demeureront en tous temps la propriété des designers, ne pourront en aucun cas être utilisés sans leur autorisation écrite et les plans devront être retournés à la terminaison du contrat.

ASSOCIATION PROFESSIONNELLE

2025

Julie Prévost-Hilaire


#1720

DESIGNERS D'INTÉRIEUR DU QUÉBEC

JPH design d'intérieurs

Julie Prévost-Hilaire
Designer d'intérieurs certifiée APDIQ ®
9165 Christophe Colomb
Montréal, Qc H2M 1Z6
514-705-5545
jphdesigner5@gmail.com

PROJET			
CENTRE EATON 705 rue STE-CATHERINE Ouest, MONRTÉAL, QC H3B 4G5 LOCAL 2570, NIVEAU MÉTRO (988 p²)			
TITRE DU DESSIN			
PLAN DE L'AMÉNAGEMENT PRÉLIMINAIRE			
DESSINÉ PAR	DATE	FEUILLE NO. 5 7	
JPH - HV	05-08-2025		
PROJET NO.	ECHELLE		
2025-06	INDIQUÉ		

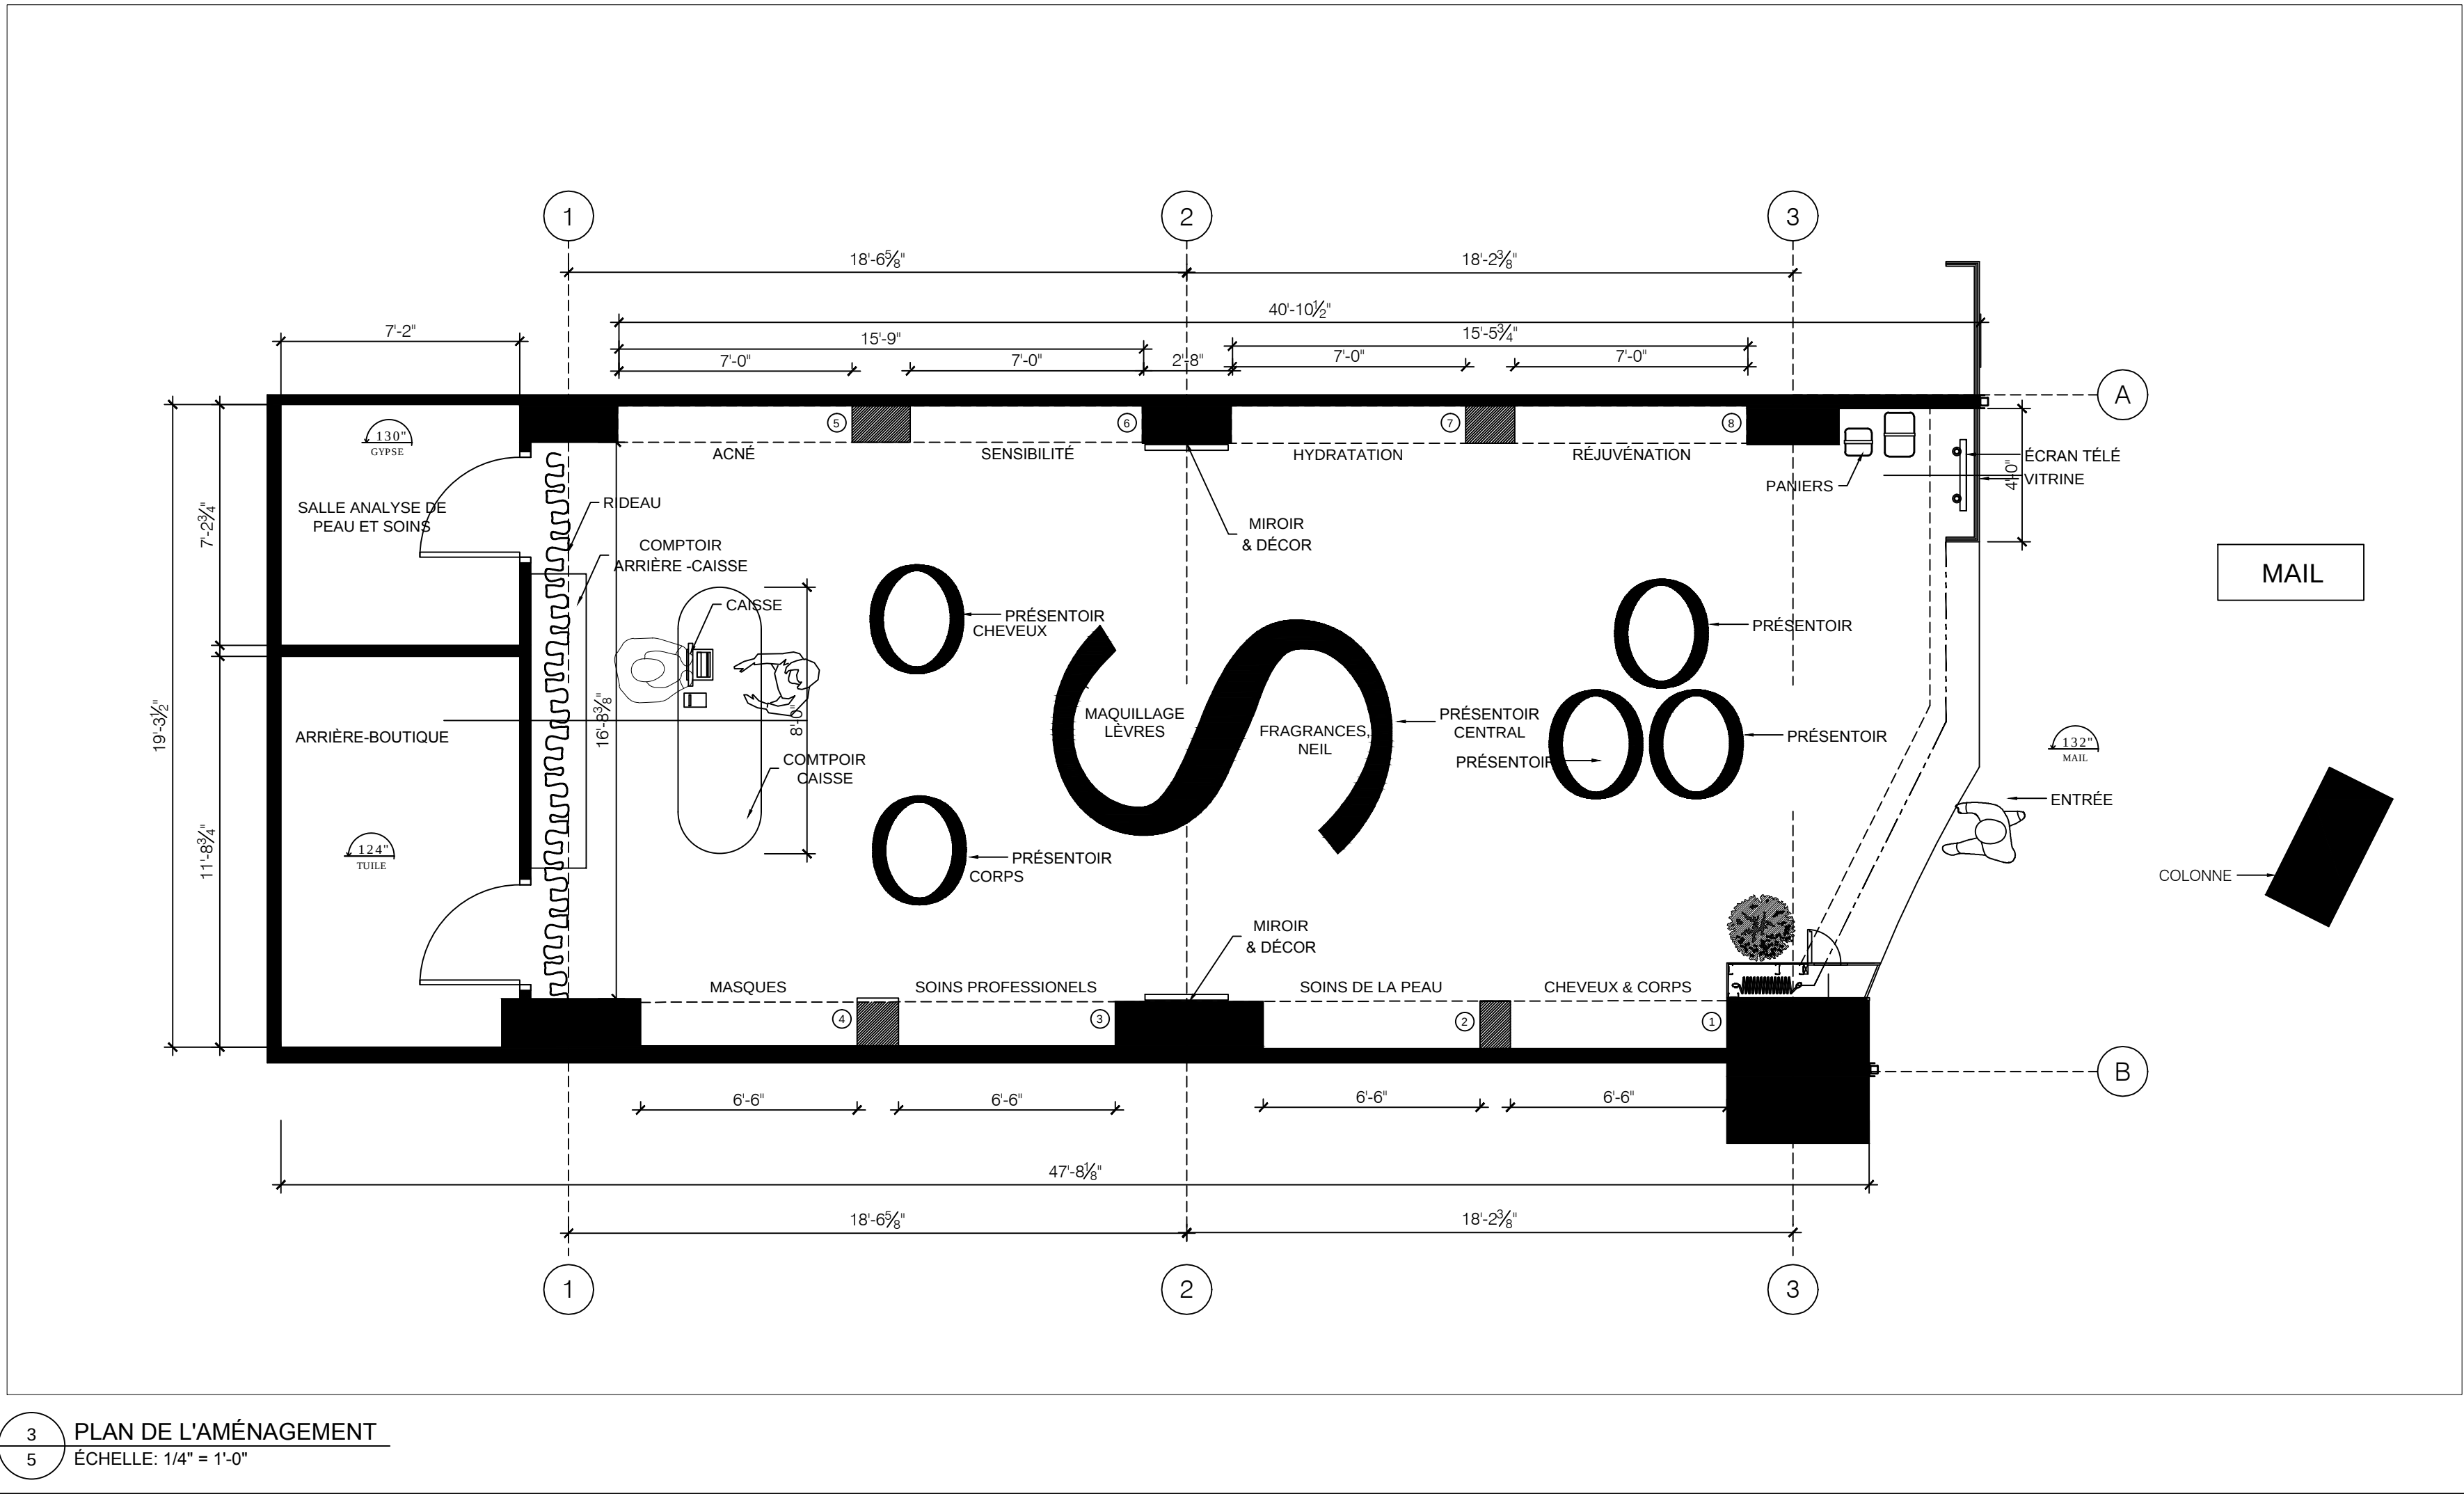

3 PLAN DE L'AMÉNAGEMENT
5 ÉCHELLE: 1/4" = 1'-0"